

**DRIVEWAY/ENCROACHMENT PERMIT
YUBA COUNTY DEPARTMENT OF PUBLIC WORKS**

ENCR26-0043

915 8th Street, Suite 125

Marysville, CA 95901

PHONE: (530) 749-5420 FAX: (530) 749-5424

In compliance with your application for the work located in Yuba County:

987 COUNTRY CLUB ROAD

ARBOGA, CA 95961

APN No. : 014370041000

TO PERMITTEE:

Owner:

987 COUNTRY CLUB ROAD
ARBOGA, CA 95961

Applicant:

Permit Manager
1170 Howell Mill Road #210 #210
GA 30318
(714) 865-4101

Gen. Contractor:

Sub-Contractor:

and subject to the following, PERMISSION IS HEREBY GRANTED to:

Install (1) solar powered License Plate Reader camera on 14' aluminum pole(s) with 30" concrete foundation in the ROW on behalf of Yuba County Sheriffs Office

Estimated Work:

The encroachment permit is limited to the following work:

Other (estimated work): Camera installation

Any work not specifically described in the encroachment permit shall require an encroachment permit amendment or the issuance of a new permit.

Drainage Req.:

Construction Req.:

This permit is subject to modification or change at any time by Yuba County Public Works to meet public safety or Yuba County standards.

Schedule a pre-construction meeting with Public Works Inspection (two business days' notice is required) prior to beginning construction

Traffic control to conform with current CA Manual of Uniform Traffic Control Devices

Surface Req.:

Applicant shall notify Underground Service alert at least 48 hours prior to excavation by calling 1 (800) 227-2600. All construction materials and workmanship shall conform to the latest edition of the Yuba County Improvement Standards, the latest edition of the State of California Department of Transportation Standard Specifications, and other agencies' Standards as applicable.

Before starting work, the permittee shall notify Yuba County Department of Public Works **Inspection, (530)749-5656**, two working days in advance of the date work is to begin and prior to final inspection. See General Provisions for delay. Attention is directed to the General Provisions and to any specific conditions attached hereto and made a part hereof.

All work shall be conducted and completed to the satisfaction of Public Works Representatives.

Work conducted under this encroachment permit shall be conducted in compliance with all applicable requirements of the National Pollutant Discharge Elimination System (NPDES), to govern the discharge of storm water and non-storm water from its properties. Work shall also be in compliance with all other applicable Federal, State and Local Laws and regulations. **If this permit is in conjunction with a building permit, all work required by this permit must be completed and approved by Yuba County Department of Public Works Inspection before Building Department Final is Scheduled.**

Issued By: Vanessa Solorio Date: 2/11/2026

Final Approval: _____ Date: _____

Upon Signature,

Applicant and/or Owner agrees to abide by the conditions of this permit, its provisions and gives County personnel the authority to inspect all on-site improvements outside the County right of way. Applicant also agrees to save and hold harmless the County and each and every officer and employee thereof from any liability or responsibility for any accident, loss or damage to persons or property arising out of or connected in any way with any work done by the applicant under any permit granted hereunder. Applicant also acknowledges that the permit will expire within 18 months if construction has not been completed and no extension has been requested.

Signature Crystal Braun

Date: 2/11/2026

**Know what's below.
Call before you dig.**

811

Now there's a new, national number that will connect you to your local One-Call Center. Before you dig, simply call 811. Or call 1-800-227-2600 to connect directly to USA North, the One-Call Center proudly serving Central and Northern California and all of Nevada.

1-800-227-2600

Call two working days before you dig

It's the law and it's FREE

Whether you're a homeowner or professional excavator, if you're going to dig you must call USA North – the one call center serving Northern and Central California and Nevada. Excavations in California and Nevada require a full two (2) working day notice. In addition to your personal safety and the safety of others, calling before you dig is about protecting the vital buried facilities that supply electric, gas, water, cable and more to our homes, schools, facilities and businesses. Remember, it's the law and it's free.



**Let's all do our part to protect our vital buried facilities.
Please take a flyer and color code booklet with you.**

For more information, visit USA North online at www.usanorth.org

Dig Safely.

5 STEPS TO A SAFE EXCAVATION

1. Survey & Mark

Survey your proposed excavation site. Make a list of affected owner/operators of underground facilities (owner/operators) at your job site, their needs and requirements. Mark the excavation site on paved surfaces with white spray chalk paint; use flags, stakes, whiskers, etc. on unpaved surfaces. (Homeowners can use flour).

2. Call Before You Dig

Call USA North 2 working days before you dig in California and Nevada. Only owner/operators who are members of the USA North program will be notified. USA North accepts design stage requests through its Internet access only, call 925-798-9504 ext 0 for more information. Emergency calls are not accepted in California. In case of a life-threatening situation, call 911 or your local fire department. Compare your list of affected owner/operators determined in Step 1, with the list of owner/operators notified by USA North. For your safety, contact any owner/operator at your job site that is not a member of USA North.

3. Wait The Required Time

The 2 working day notice in CA & NV allows USA North members to examine their underground facility records and respond to you. Our members, who are owner/operators of underground facilities, will provide you information about the location of their facility, mark, or stake the horizontal path of their facility with the appropriate color code, or advise of clearance. Depending on our member's workload, they may contact you to try to negotiate a new start time for your excavation. This will allow them the opportunity to provide you with greater service.

4. Respect The Marks

Preserve facility marks for the duration of the job. If any of the owner/operator markings are not reasonably visible, you must call USA North and request re-marking by the affected owner/operator(s). A re-mark request requires a 2 working day notice in CA & NV. When you request a owner/operator(s) to re-mark their facilities, you will be asked if your excavation site is still outlined in white spray chalk, so the USA North members can respond to your request. Your ticket is active for 28 calendar days in CA and 14 calendar days in NV from the date of your call to USA North. You must have an active USA North ticket for the entire duration of your excavation.

5. Dig With Care

In California hand excavate within 24" of the outside diameter of the facility – in Nevada, 30". Facilities that are in conflict with your excavation are to be located by hand and protected before power equipment is used. Notify the affected utility of any contact, scrape, dent, nick or damage to their facility.

Refer to California Government Code 4216 and Nevada Regulatory Statute 455.080 - 455.180 for liability risks. There are fines of up to \$50K and \$100K respectively for violations of these state laws.

USA NORTH

4090 Nelson Avenue, Suite A • Concord, CA 94520-1232

Call 6:00 A.M. - 7:00 P.M. (PT) • Monday - Friday

Dig Safely.

www.usanorth.org

YUBA COUNTY DEPARTMENT OF PUBLIC WORKS

DRIVEWAY CONSTRUCTION & ENCROACHMENT PERMIT GENERAL PROVISIONS

1. AUTHORITY:

Each permit is issued in accordance with Chapter 5.5 of Division 2, commencing with Section 1450 et seq., of the Streets and Highways Code (SHC) and Yuba County Ordinance Code, Chapter 9.50 and 11.52.

2. REVOCATION:

Except as otherwise provided for public corporations, franchise holders, and utilities, permits are revocable on five (5) days notice. These General Provisions, Utility Maintenance Provisions, and any permit issued hereunder are revocable or subject to modification or abrogation at any time without prejudice, however, to prior rights, including those evidenced by joint use agreements, franchise rights, reserved rights, or any other agreements for operation purposed in the County highway right-of-way.

3. RESPONSIBLE PARTY:

No party other than the named permittee or their agent is authorized to work under any permit.

4. ACCEPTANCE OF PROVISIONS:

It is understood and agreed by the permittee that doing of any work under this permit shall constitute an acceptance of the provisions of this permit and all attachments.

5. NOTICE PRIOR TO STARTING WORK:

Before starting work under the permit, the permittee shall notify the designated department representative two (2) working days prior to initial start of work. When work has been interrupted for more than five (5) working days, an additional notification is required before restarting work unless a pre-arranged agreement has been made with the department's representative. Unless otherwise specified, all work shall be performed on weekdays and during normal working hours of the department's representative.

6. STANDARDS OF CONSTRUCTION:

All work performed within the highway shall conform to the latest edition of the Yuba County Improvement Standards and the current California Department of Transportation Standard Specifications and any Special Provisions relating thereto.

7. INSPECTION AND APPROVAL BY THE DEPARTMENT:

All work shall be subject to monitoring, inspection, and approval by the Department. The permittee shall request a final inspection and acceptance of the work.

8. KEEP PERMIT ON THE WORK SITE:

The permit or a copy thereof shall be kept at the site of the work and must be shown to any representative of the department or any law enforcement officer on demand. WORK SHALL BE SUSPENDED IF PERMIT IS NOT AT JOB SITE AS PROVIDED.

9. CONFLICTING PERMITS:

If a prior encroachment conflicts with the proposed work, the new permit tee must arrange for any necessary removal or relocation with the prior permit tee. Any such removal or relocation will be at no expense to the department.

10. PERMITS FROM OTHER AGENCIES:

The party or parties to whom a permit is issued shall, whenever required by law, secure the written authorization for any work that must be approved by the Public Utilities Commission (PUC) of the State of California, CAL-OSHA, or any other public agency having jurisdiction. Failure to comply with the law, as noted above, will invalidate the department's permit.

11. PROVISIONS FOR PEDESTRIANS:

Where facilities exist, a minimum sidewalk and bike path width of four feet (4) shall be maintained at all times for safe passage through the work area. At no time shall pedestrians be diverted onto a portion of the street used for vehicular traffic. At locations where adjacent alternate walkways cannot be provided, appropriate signs and barricades shall be installed at the limits of construction and in advance of closure at the nearest crosswalk or intersection to divert pedestrians across the street.

12. PROTECTION OF TRAFFIC:

Adequate provisions shall be made for the protection of the traveling public. Warning signs, lights and safety devices, shall conform to the requirements of the Manual of Traffic Controls issued by the California Department of Transportation. Traffic control for day or nighttime lane closures shall be in conformance with California Department of Transportation Standard Plans for Traffic Control Systems. Nothing in the permit is intended, as to third parties, to impose on permittee any duty, or standard of care, greater than or different than the duty or standard of care imposed by law.

13. MINIMUM INTERFERENCE WITH TRAFFIC:

All work shall be planned and carried out so that there will be the least possible inconvenience to the traveling public. The permittee is authorized to place properly attired flagger(s) to stop and warn conventional highway traffic. Traffic shall not be unreasonably delayed. Flagging procedures shall be in conformance with the Instructions to Flaggers pamphlet and/or Manual of Traffic Controls for Construction and Maintenance Work Zones issued by the Department. A traffic control plan shall be submitted to the County for comment.

14. STORAGE OF EQUIPMENT AND MATERIAL:

No material shall be stored within eight (8) feet of the edge of the pavement or traveled way or within the shoulder lines where the shoulders are wider than eight (8) feet. Utilities are subject to the provisions of Section 22512 of the California Vehicle Code (CVC).

15. CARE OF DRAINAGE:

If the work contemplated in any permit shall interfere with the established drainage, ample provision shall be made by the permittee to provide for it as may be directed by the department.

16. MAKING REPAIRS:

In every case, the permittee shall be responsible for restoring to its former condition as nearly as may be possible any portion of the County highway facility which has been excavated or otherwise disturbed by permittee. The permittee shall maintain the surface over facilities placed under any permit. If the highway is not restored as herein provided for, or if the department elects to make repairs, permittee agrees by acceptance of permit to bear the cost thereof.

17. CLEAN UP RIGHT-OF-WAY:

Jobsite and right of way shall be kept clean at all times. Upon completion of the work all brush, timber, scraps, material, etc., shall be entirely removed and the County right-of-way shall be left in as presentable a condition as existed before work started.

18. COST OF WORK:

Unless otherwise stated on the permit or other separate written agreement, all cost incurred for work within the County right-of-way pursuant to this permit shall be borne by the permittee, and permittee hereby waives all claims for indemnification or contribution from the County for such work.

19. ACTUAL COST BILLING:

When the permittee is to be billed actual costs (as indicated on the face of the permit), such costs will be at the current hourly rate established by the department for permits.

20. SUBMIT PLAN:

For installation of all underground facilities, and all surface work or other activity of consequence, the permittee shall furnish two (2) sets of plans showing location and construction of other activity with its application. Prior to acceptance of the work, one (1) set of as-built plans shall be submitted to the Department of Public Works.

21. BONDING:

This permit shall not be effective for any purpose unless, and until the permittee files with the department a surety bond when required by the department in the form and amount required by the department. A bond is not ordinarily required of any public corporation or publicly or privately-owned utility but will be required of any utility that fails to meet any obligation arising out of the work permitted or done under a permit or fails to maintain its plant, work, or facilities. The said bond shall remain in force for a period of one (1) year after acceptance of the work by the department.

22. MAINTENANCE OF HIGHWAYS:

The permittee agrees, by acceptance of a permit, to properly maintain any encroachment. This will require inspection and repair of any damage to County facilities resulting from the encroachment.

23. RESPONSIBILITY FOR DAMAGE:

The County of Yuba and all officers and employees thereof, including but not limited to the Director of Public Works and the Deputy Director, shall not be answerable or accountable in any manner for injury to or death of any person, including but not limited to the permittee, persons employed by the permittee, persons acting in behalf of the permittee, or for damage to property from any cause. The permittee shall be responsible for any liability imposed by law and for injuries to or death of any person, including but not limited to the permittee, persons employed by the permittee, persons acting in behalf of the permittee, or damage to property arising out of work, or other activity permitted and done by the permittee under a permit, or arising out of the failure on the permittee's part to perform his obligations under any permit in respect to maintenance or any other obligations, or from any cause whatsoever during the progress of the work, or other activity, or at any subsequent time work or other activity is being performed under the obligations provided by and contemplated by the permit. The permittee shall indemnify and save harmless the County and all officers and employees thereof, including but not limited to the Director of Public Works and the Deputy Director, from all claims, suits or actions of every name, kind and description brought for or on account of injuries to or death of any person, including but not limited to the permittee, persons employed by the permittee, persons acting in behalf of the permittee and the public, or damage to property resulting from the performance of work or other activity under the permit, or arising out of the failure on the permittee's part to perform his obligations under any permit in respect to maintenance or any other obligations, or resulting from defects or obstructions, or from any cause whatsoever during the progress of the work, or other activity or at any subsequent time work or other activity is being performed under the obligations provided by and contemplated by the permit, except as otherwise provided by statute. The duty of the permittee to indemnify and save harmless includes the duties to defend as set forth in Section 2778 of the Civil Code. The permittee waives any and all rights to any type of expressed or implied indemnify against the County its officers or employees. It is the intent of the parties that the permittee will indemnify and hold harmless the County its officers and employees from any and all claims, suits or actions as set forth above regardless of the existence or degree of fault or negligence, whether active or passive, primary or secondary, on the part of the County the permittee, persons employed by the permittee, or persons acting in behalf of the permittee.

24. NO PRECEDENT ESTABLISHED:

This permit is issued with the understanding that any particular action is not to be

considered as establishing any precedent (1) on the question of the expediency of permitting any certain kind of encroachment to be erected within right-of-way of County highways, or (2) as to any utility of the acceptability of any such permits as to any other or future situation.

25. ARCHAEOLOGICAL:

The permittee shall cease work in the vicinity of any archaeological resources that are revealed. The Permit Engineer shall be notified immediately. A qualified archaeologist, retained by the permittee, will evaluate the situation and make recommendations to the Permit Engineer concerning the continuation of the work.

26. FUTURE MOVING OF INSTALLATIONS:

If the Encroachment Permit was issued at the request of the permittee, it is understood that whenever County construction, reconstruction or maintenance work on the highway requires the installation to be moved, adjusted or relocated, the permittee, at his sole expense, upon request of the department, shall comply with said request.

27. RIGHT OF ENTRY:

By signing the Permit Application, the applicant agrees to allow County Personnel right of entry to the property to inspect project site.

28. DEVIATIONS:

The permittee shall notify the department in writing of any proposed deviations or changes in the work to be done under any permit and shall not proceed therewith until he has obtained both the written consent of the department, and the written, signed and acknowledged consent to such deviation or change of any surety company whose bond or bonds are posted in connection with such work.

29. CHANGES ON PERMITS:

Any permit issued hereunder shall be subject to such conditions, changes or limitations as are from time to time deemed necessary by the department for the protection of the highways or to prevent undue interference with the traffic or to protect both persons and property within, upon or adjacent to the highways from damage or danger. In the case of changes or limitations or conditions to be made or imposed by the department after a permit is issued hereunder, the department shall notify the permittee thereof, in writing, either by mail to the address set forth on the application or by personal service upon the permittee. Such change in new limitation or condition shall be effective twenty-four (24) hours after deposit in the United States mail or immediately upon personal service.

30. PRESERVATION OF MONUMENTS:

Any monument set for the purpose of locating or preserving the lines of any road or property subdivisions, or a precise survey reference point, or a permanent survey bench mark within the county shall not be removed or disturbed or caused to be removed or disturbed without first obtaining permission in writing from the department to do so. Before monuments, reference points and bench marks are disturbed, or removed, they shall be tied out by a licensed surveyor or registered civil

engineer or under the directions of same. After completion of the work, the monuments, reference points and bench marks shall be accurately reset at the expense of permittee.

31. PROTECTION OF ADJOINING PROPERTY:

The permittee shall at all times and at his own expense preserve and protect from injury any adjoining property by providing proper foundations and taking other measures suitable for the purpose. Where in the protection of such property it is necessary to enter upon private property for the purpose of taking appropriate protective measures the permittee shall first attempt to obtain a license from the owner of such private property for such purposes. The permittee shall, at his own expense, shore up and protect all buildings, walls, fences or other property likely to be damaged during the progress of the excavation work and shall be responsible for all damage to any roads or other public or private property, real and personal, resulting from his failure properly to protect and carry out such work subject to the foregoing provisions relating to entry upon private property. Whenever it is necessary to trench through any lawn area, the permittee shall carefully cut the sod and upon completion of the work shall replace it or reseed the area if cutting a replacing sod is impractical. All construction and maintenance work shall be done in a manner calculated to leave the lawn area clean of earth and debris and in a condition as close as possible to that which existed before such work began. The permittee shall not remove, even temporarily, any trees, or shrubs which exist in parking strip areas without first obtaining the consent of the department or other county officials having control of such property.

32. SAVE HARMLESS AGREEMENT:

The permittee agrees to save and hold harmless the County and each and every officer and employee thereof from any liability or responsibility for any accident, loss or damage to persons or property arising out of or connected in any way with any work done by the permittee under any permit granted hereunder.

33. DISCLAIMER OF LIABILITY:

These provisions shall not be construed as imposing upon the County or any official or employee any liability or responsibility for damages to any person injured by the performance of any work for which the permit is issued hereunder, nor shall the County or any official or employee thereof be deemed to have assumed any such liability or responsibility by reason of inspections authorized hereunder, the issuance of any permit or the approval of any work permitted hereunder.


STATE OF CALIFORNIA
YUBA COUNTY
SUBMITTED BY YUBA COUNTY SHERIFF'S OFFICE
AUTOMATIC LICENSE PLATE READING
(ALPR) CAMERA PERMIT



LOCATION / VICINITY MAP

INDEX OF DRAWING:

- SHEET 1 : COVER SHEET AND CAMERA LOCATION MAP
- SHEET 2 : GENERAL NOTES AND TRAFFIC DESIGN TABLES
- SHEET 3 : CAMERA LOCATION INFORMATION
- SHEET 4 : SITE PLAN
- SHEET 5 : TRAFFIC CONTROL PLAN
- SHEET 6-8 : POLE DETAILS

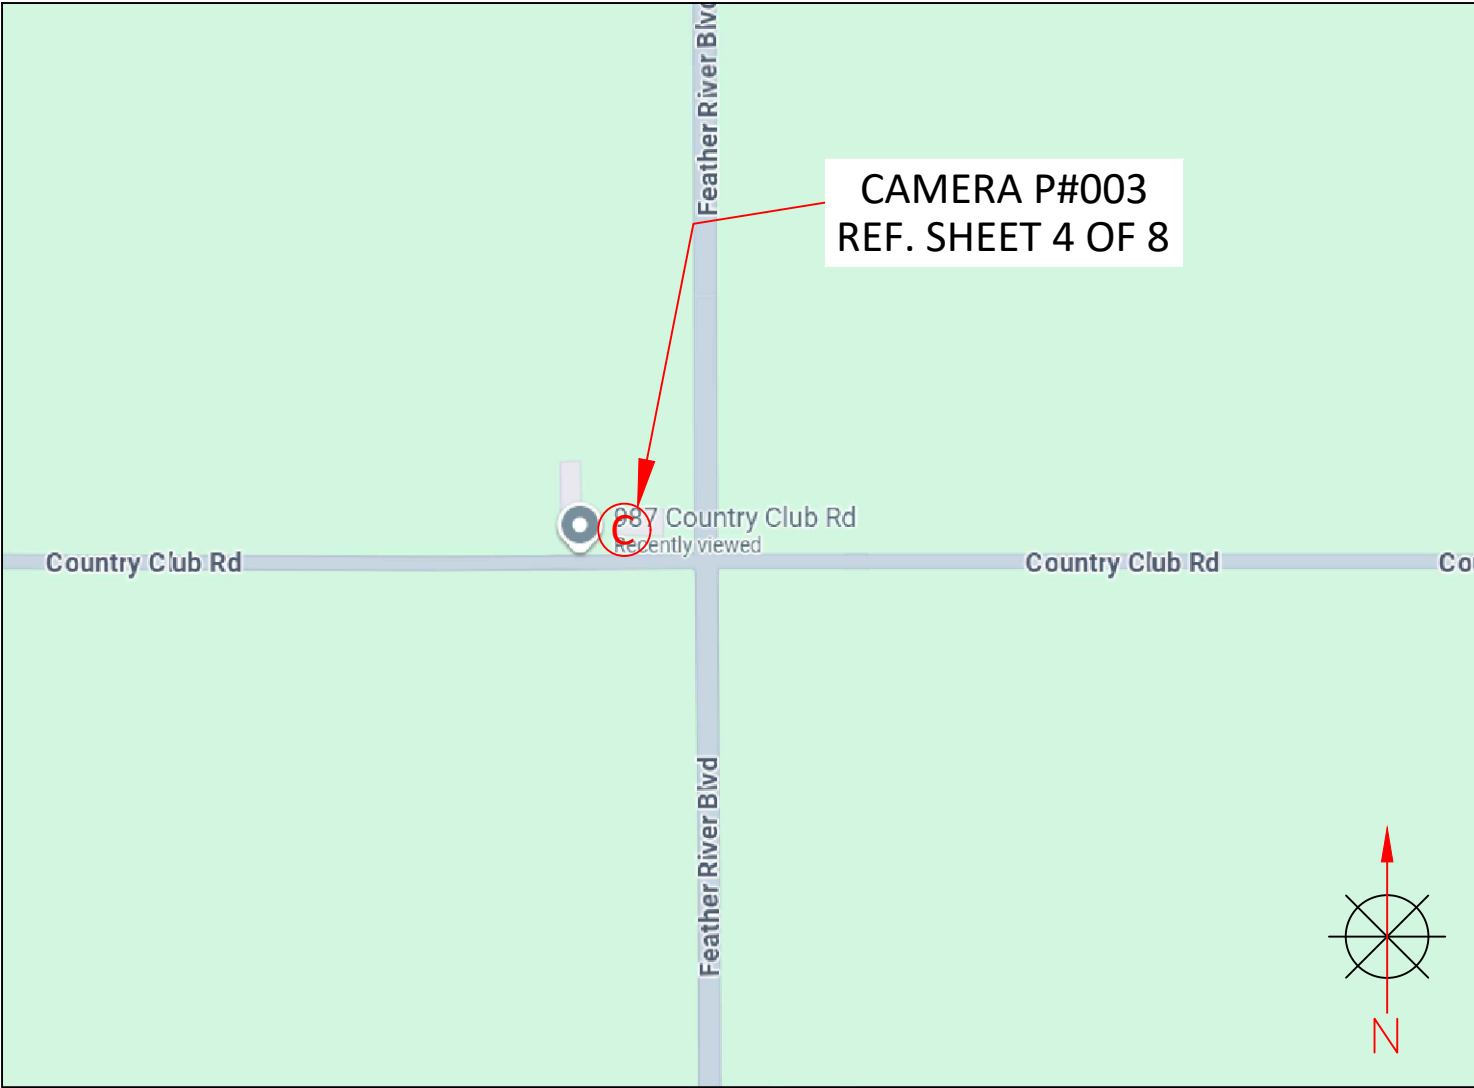

flock safety	REV	DESCRIPTION	DATE	BY	TITLE: COVER SHEET AND CAMERA LOCATION MAP	PLANS PREPARED BY: CHC A CONGRUEX COMPANY PO Box 59028 Norwalk, CA 90652 (949) 250-0004	PROJ#: 1441086	
					SCOPE OF WORK: COUNTY OF YUBA, CA ALPR CAMERA INSTALLATION		DRAWN BY: JEEVESH OJHA	
							CHECKED BY: GURKAMAL PREET SINGH	
							APPROVED BY: CRYSTAL BRAUN	
							DATE: 12/24/2025	SHEET: 1 OF 8

GENERAL NOTES AND TRAFFIC DESIGN TABLES

1. TRAFFIC CONTROL PLAN SHALL CONFORM TO THE MOST CURRENT CALIFORNIA MANUAL ON UNIFORM TRAFFIC CONTROL DEVICES FOR STREETS AND HIGHWAYS AND STATE STANDARD PLANS.
2. NO LANE CLOSURES PERMITTED BEFORE 9:00AM AND AFTER 3:00PM.
3. ALL AFFECTED RESIDENTS, BUSINESSES, AGENCIES, AND SCHOOLS SHALL BE GIVEN A 72 HOURS NOTICE PRIOR TO THE START OF WORK AND THEIR ACCESS SHALL BE MAINTAINED AT ALL TIMES.
4. TEMPORARY NO PARKING SIGNS SHALL BE POSTED 48 HOURS PRIOR TO START OF WORK.
5. ALL CONFLICTING SIGNS, STRIPING OR PAVEMENT MARKINGS SHALL BE COVERED OR REMOVED AND REPLACED WHEN WORK IS COMPLETED.
6. TRAFFIC DIRECTION THROUGH A SIGNALIZED INTERSECTION SHALL BE CONDUCTED BY THE COUNTY OF YUBA UNIFORMED POLICE OFFICER OR A COMMUNITY SERVICE OFFICER ONLY. SHOULD WORK REQUIRE A SIGNAL TO BE OVERRIDDEN, ARRANGEMENT SHALL BE MADE WITH THE CITY POLICE DEPT AND TRANSPORTATION ENGINEERING DEPT AT LEAST 14 DAYS PRIOR TO START OF WORK.

Table A - Recommended Advance Warning Sign Spacing

Posted Speed Distance Between Signs **

POSTED SPEED	A	B	C
Urban 25 mph or less***	100	100	100
Urban more than 25 mph to 40 mph***	250	250	250
Urban more than 40 mph***	350	350	350
Rural	500	500	500
Expressway/Freeway	1,000	1,500	2,640

Table B - Taper Length Criteria for Temporary Traffic Control Zones

Type of Taper	Taper Length (L)
Merging Taper	at least L
Shifting Taper	at least 0.5L
Shoulder Taper	at least 0.33L
One-Lane, Two-Way Traffic Taper	50 feet minimum, 100 feet maximum
Downstream taper	50 feet min., 100 feet max. per lane

Table C - Formulas for Determining Taper Lengths

Speed Limit	Taper Length (L) Feet
40 mph or less	L = WS ² /60
45 mph or more	L = WS

Where: L = taper length in feet
W = width of offset feet
S = posted speed limit, or off peak 85th- percentile speed prior to work starting. Or the anticipated operating speed in mph

Table D – Longitudinal Buffer Space or Flagger Station Spacing on Downgrades

Speed (mph)	% Downgrade (Buffer Space)			
	Level Road 0% (ft)	-3% (ft)	-6% (ft)	-9% (ft)
20	115	116	120	126
25	155	158	165	173
30	200	205	215	227
35	250	257	271	287
40	305	315	333	354
45	360	378	400	427
50	425	446	474	507
55	495	520	553	593
60	570	598	638	686
65	645	682	728	785
70	730	771	825	891

Table E – Taper Length Criteria for Temporary Traffic Control Zones
(for 12 feet Offset Width)

Speed* S (mph)	Minimum Taper Length ** For Width of Offset 12 ft (W)			
	Merging L (ft)	Shifting L/2 (ft)	Shoulder L/3 (ft)	Down Stream (ft) ***
20	80	40	27	50
25	125	63	42	50
30	180	90	60	50
35	245	123	82	50
40	320	160	107	50
45	540	270	180	50
50	600	300	200	50
55	660	330	220	50
60	720	360	240	50
65	780	390	260	50
70	840	420	280	50

Table F – Maximum Spacing of Channelizing Devices

Speed (mph)	Maximum Channelizer Spacing		
	Taper* (ft)	Tangent (ft)	Conflict** (ft)
20	20	40	10
25	25	50	12
30	30	60	15
35	35	70	17
40	40	80	20
45	45	90	22
50	50	100	25
55	55	110	27
60	60	120	30
65	65	130	32
70	70	140	35



REV	DESCRIPTION	DATE	BY

TITLE:	GENERAL NOTES AND TRAFFIC DESIGN TABLES
SCOPE OF WORK:	COUNTY OF YUBA, CA ALPR CAMERA INSTALLATION

PLANS PREPARED BY:



PROJ#: 1441086
DRAWN BY: JEEVESH OJHA
CHECKED BY: GURKAMAL PREET SINGH
APPROVED BY: CRYSTAL BRAUN
DATE: 12/24/2025 SHEET: 2 OF 8


CAMERA LOCATION INFORMATION

CAMERA NO.	LOCATION			
	STREET	DIRECTION	LATITUDE LONGITUDE	POLE
P#003	COUNTY CLUB RD.	WESTBOUND	39.033148457626300, -121.5792375115620	NEW FLOCK POLE


SITE ADDRESS:
987 COUNTRY CLUB RD, OLIVEHURST, CA 95961

SITE PLAN


LINE LEGENDS

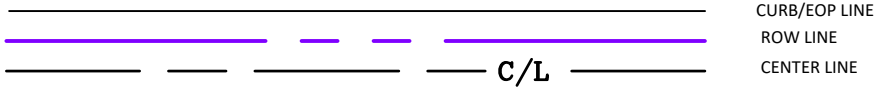

AERIAL VIEW

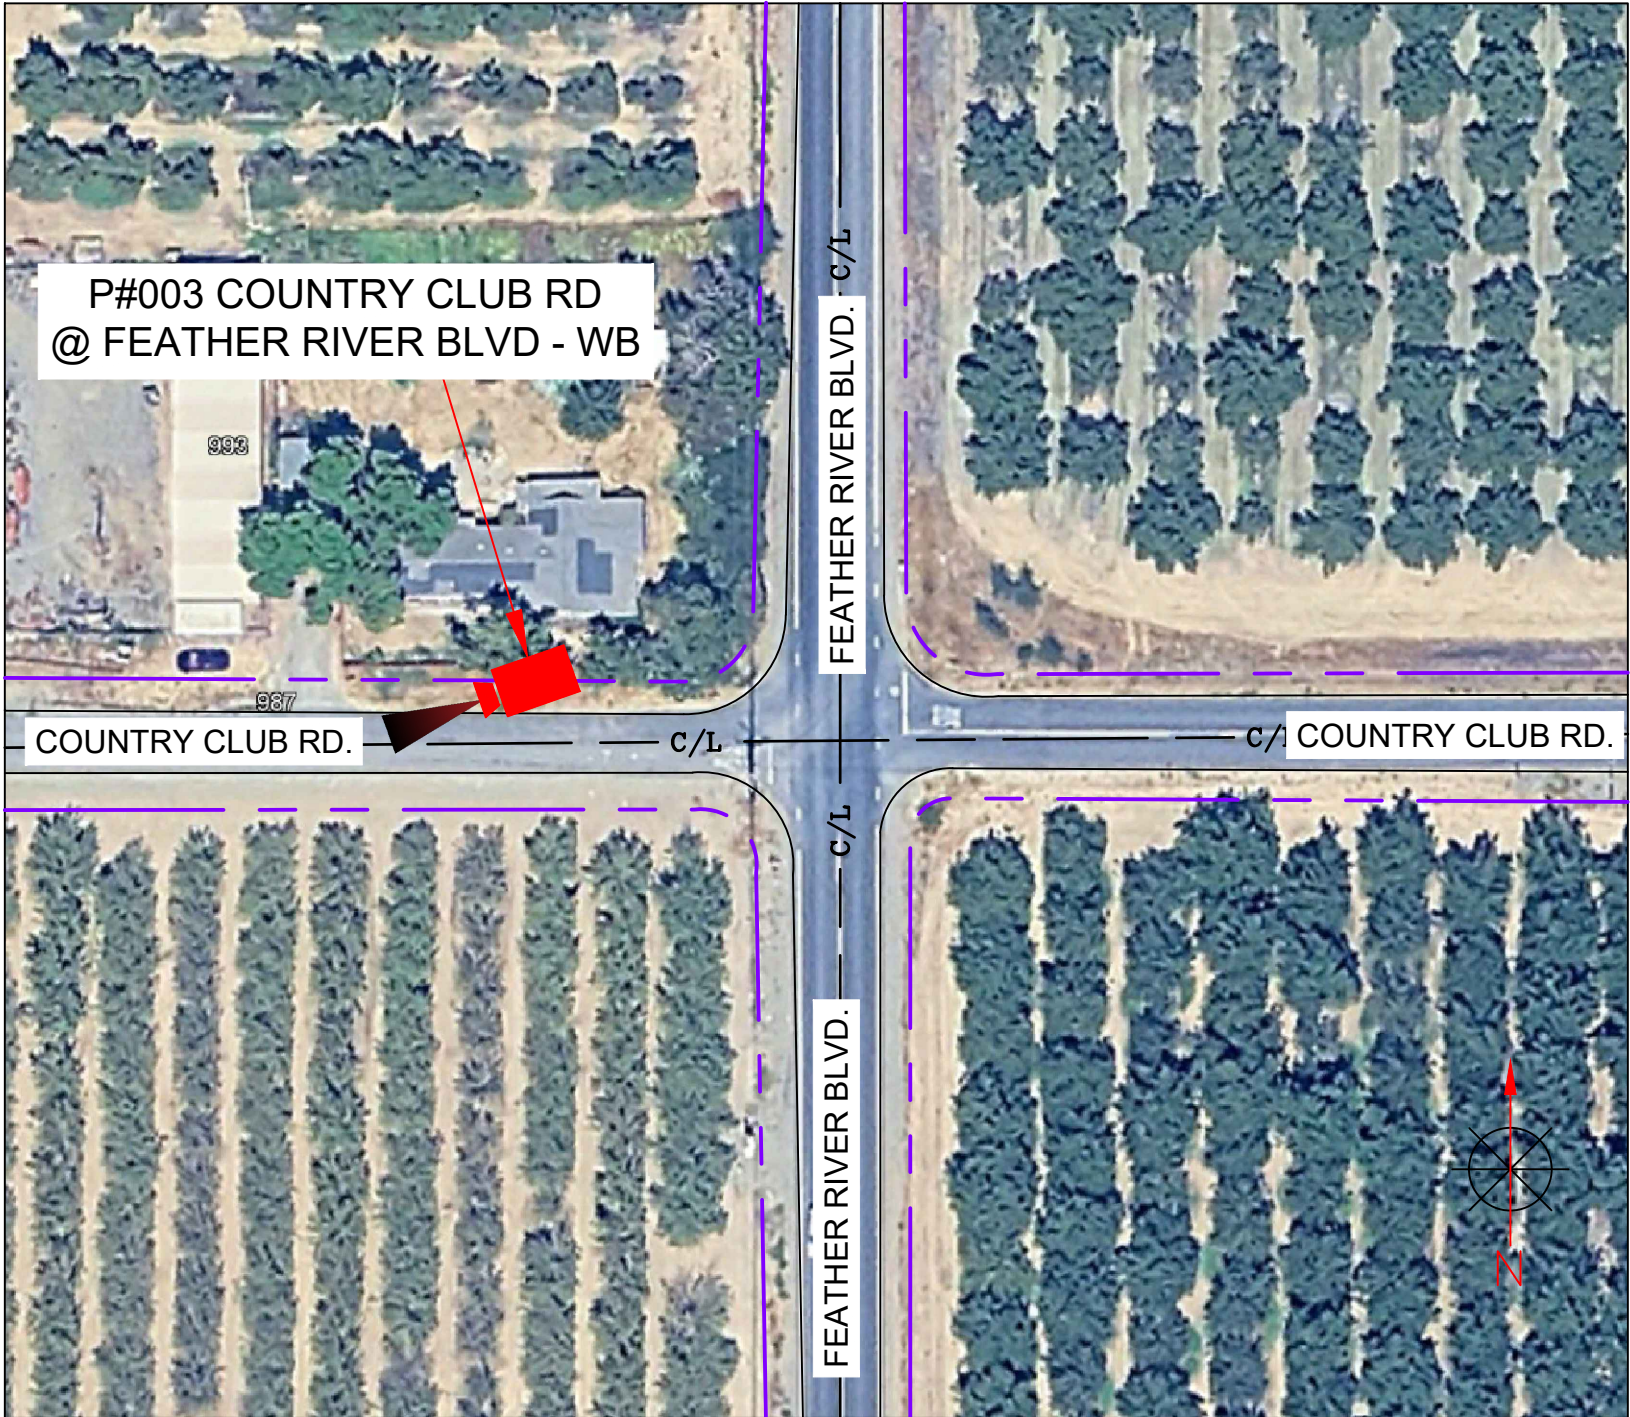

STREET VIEW

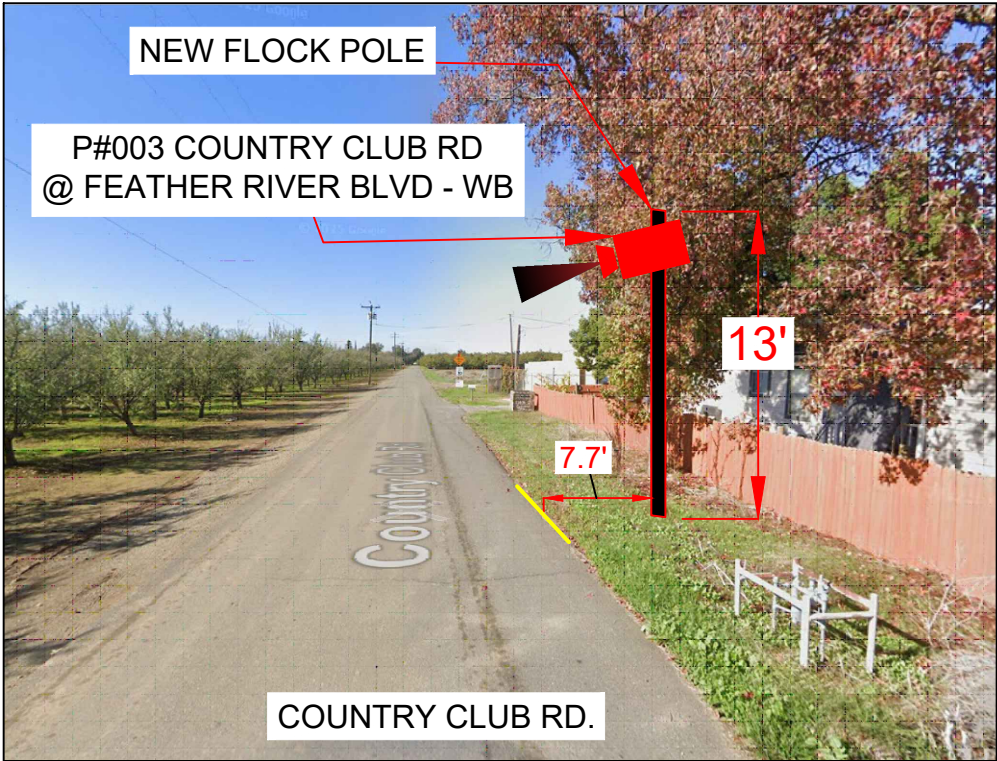

REV	DESCRIPTION	DATE	BY

TITLE:	SITE PLAN
SCOPE OF WORK:	COUNTY OF YUBA, CA ALPR CAMERA INSTALLATION


PLANS PREPARED BY:



PROJ#: 1441086

DRAWN BY:	JEEVESH OJHA
CHECKED BY:	GURKAMAL PREET SINGH
APPROVED BY:	CRYSTAL BRAUN
DATE:	12/24/2025
SHEET:	4 OF 8

987 COUNTRY CLUB RD.
COUNTRY CLUB RD. AND
FEATHER RIVER BLVD.
-ALPR CAMERA P#003 PL.
WORK AREA 1 OF 1

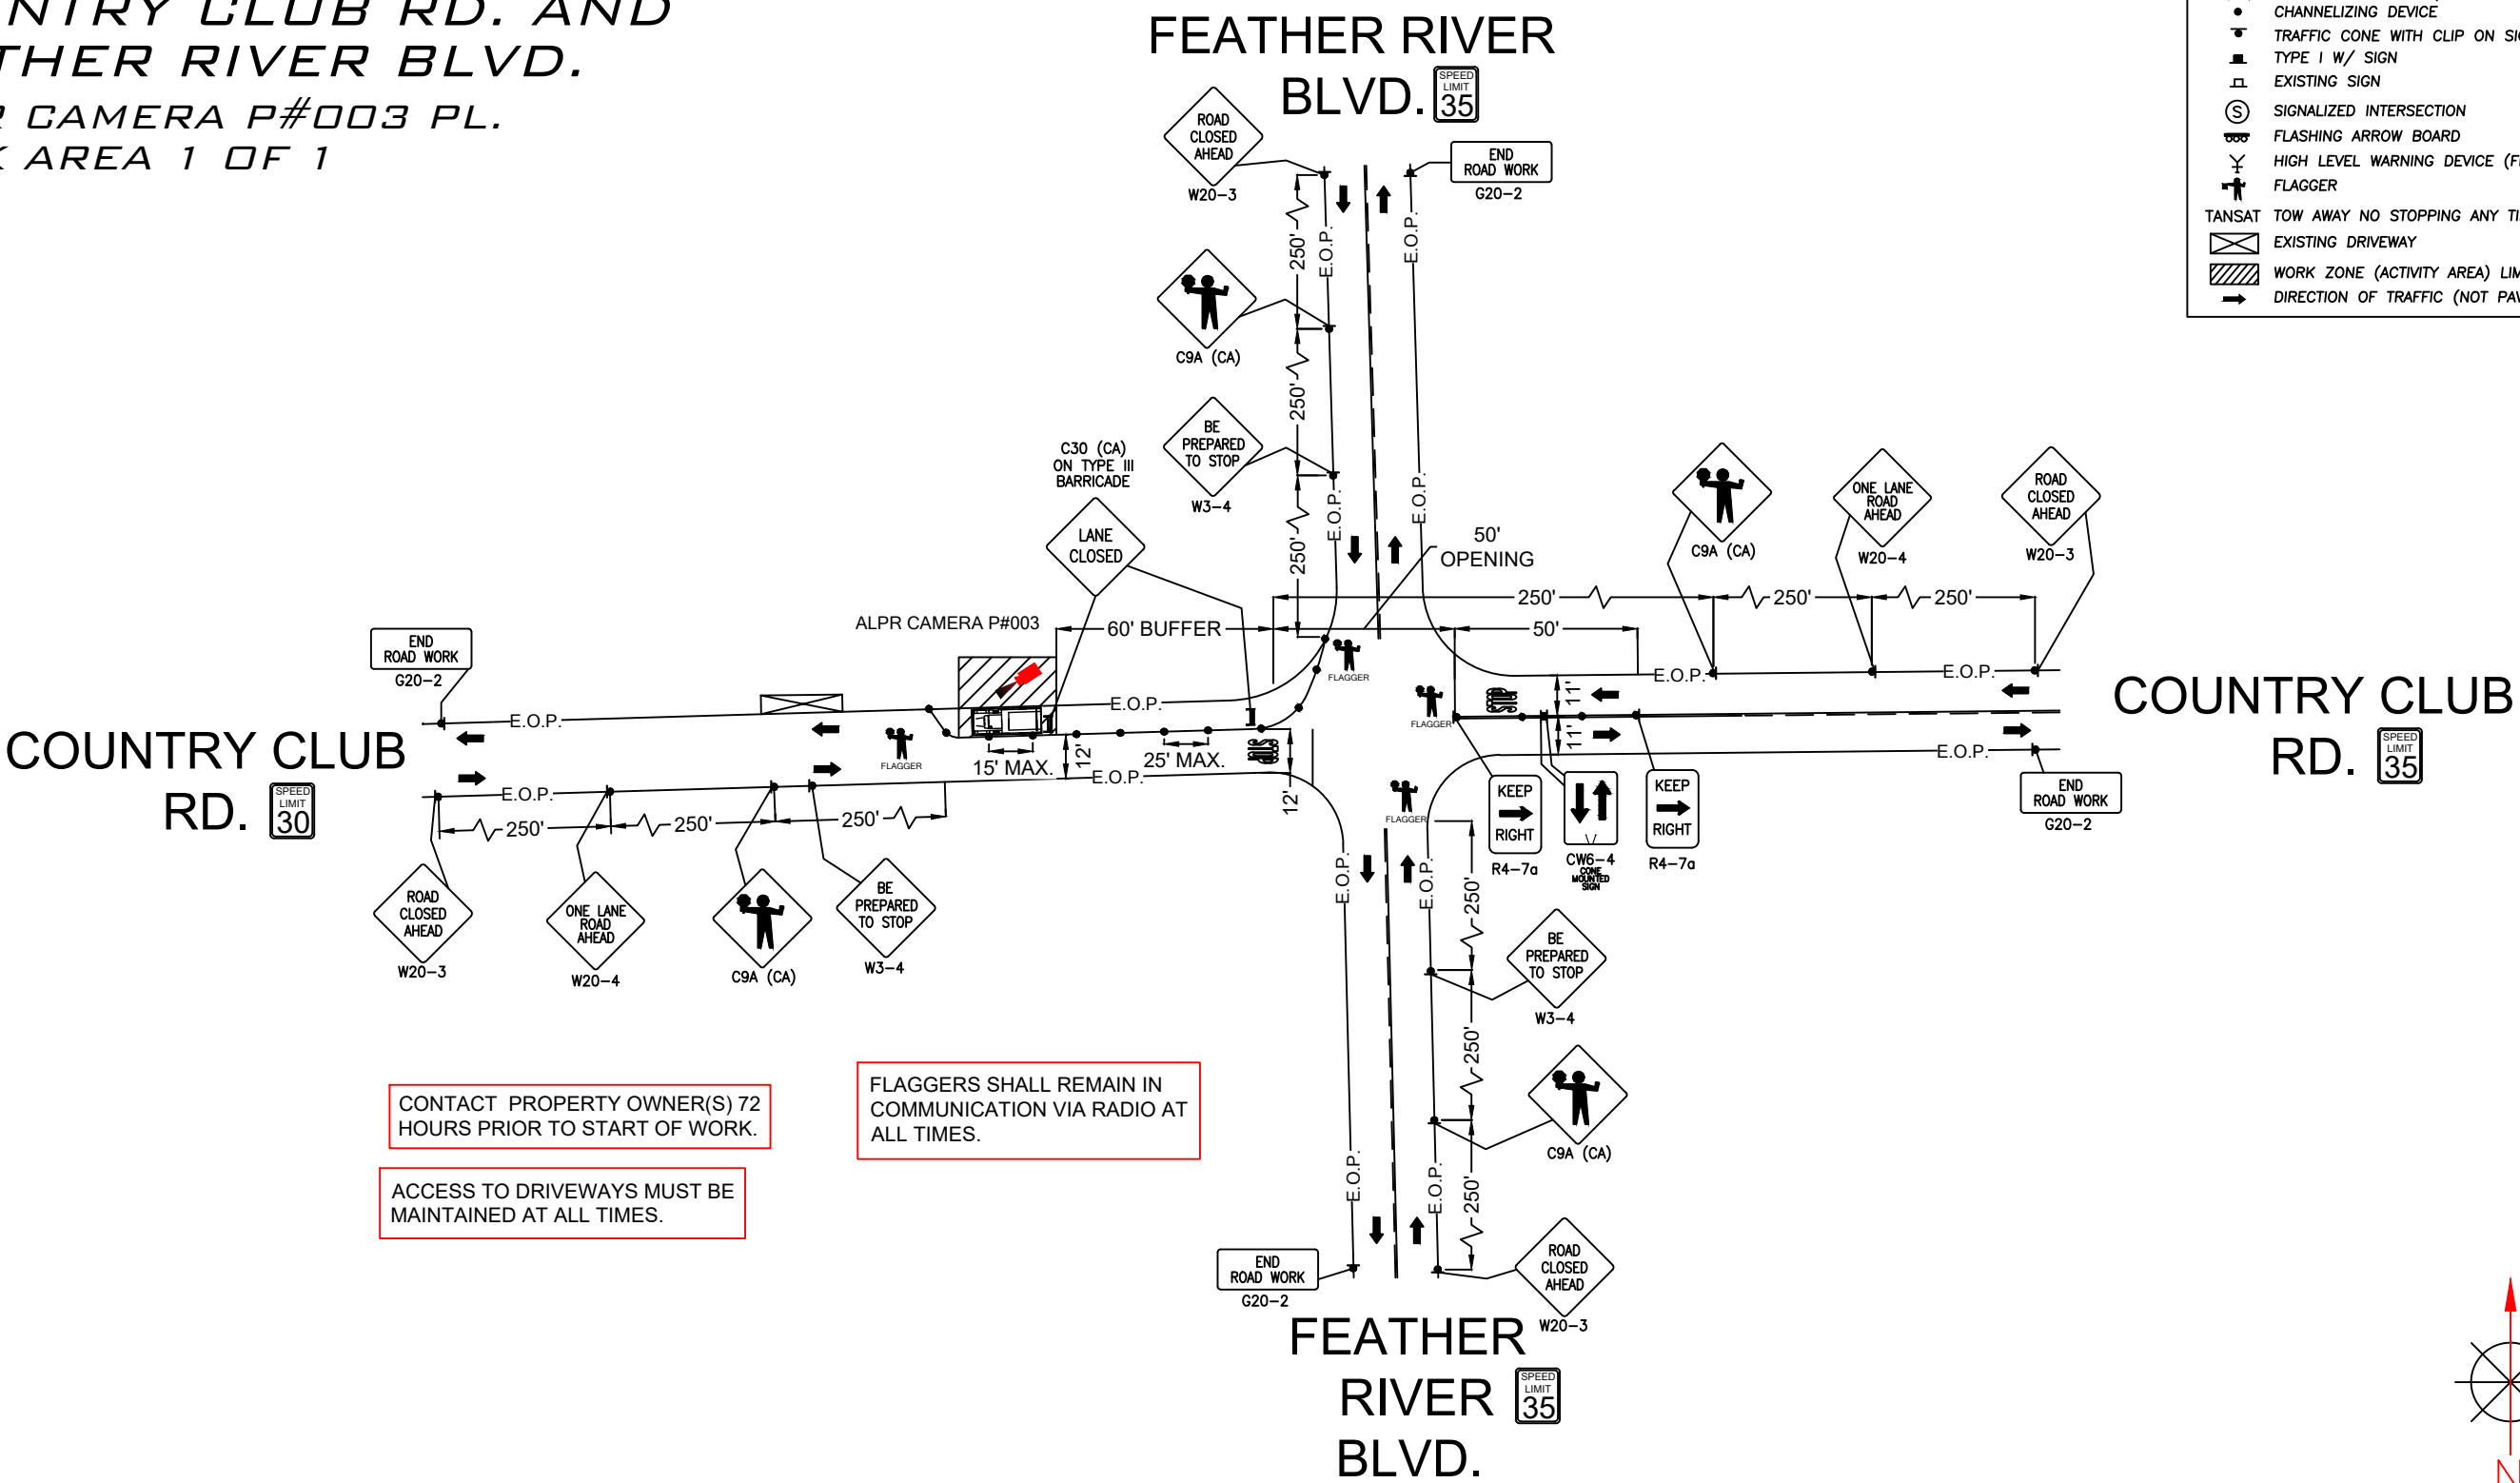

CONTACT PROPERTY OWNER(S) 72 HOURS PRIOR TO START OF WORK.

ACCESS TO DRIVEWAYS MUST BE MAINTAINED AT ALL TIMES.

FLAGGERS SHALL REMAIN IN COMMUNICATION VIA RADIO AT ALL TIMES.



REV	DESCRIPTION	DATE	BY

TITLE:	TRAFFIC CONTROL PLAN
SCOPE OF WORK:	COUNTY OF YUBA, CA ALPR CAMERA INSTALLATION

PLANS PREPARED BY:	A CONGRUEX COMPANY PO Box 59028 Norwalk, CA 90652 (949) 250-0004
--------------------	---

PROJ#:	1441086
DRAWN BY:	JEEVESH OJHA
CHECKED BY:	GURKAMAL PREET SINGH
APPROVED BY:	CRYSTAL BRAUN
DATE:	12/24/2025
SHEET:	5 OF 8

DESIGN NOTES

1. POLE AND FOUNDATIONS ARE DESIGNED IN ACCORDANCE WITH THE FOLLOWING CODES:
- 1.1. 2009/2012/2015/2018/2021 INTERNATIONAL BUILDING CODE
 - 1.2. AASHTO LRFD SPECIFICATIONSFOR STRUCTURAL SUPPORT FOR HIGHWAY SIGNS, LUMIN, TRAFFIC SIGNALS, 2015 EDITION.
2. POLE ANALYSIS AND FOUNDATION DESIGN ARE BASED ON THE FOLLOWINGCRITERIA
- 2.1. DESIGN WIND SPEED (Vult)): (SEE SECTION 2.6)
 - 2.2. RISK CATEGORY: II
 - 2.3. EXPOSURE CATEGORY: C
 - 2.4. TOPOGRAPHIC CATEGORY: 1
 - 2.5. SEISMIC DESIGN CRITERIA:
 - 2.5.1. SOIL SITE CLASS: D (ASSUMED)
 - 2.5.2. SPECTRAL RESPONSE, Ss: 1.000g (MAXIMUM)
 - 2.5.3. SPECTRAL RESPONSE, S1: 0.400g (MAXIMUM)
 - 2.5.4. SEISMIC DESIGN CATEGORY: B
 - 2.6. STRUCTURE BASE REACTIONS ARE CALCULATED AS FOLLOWS:

DESIGN WIND SPEED (MPH)	MOMENT (K-FT)	SHEAR (KIP)	AXIAL (KIP)
115	2.70	0.280	0.160
125	3.20	0.330	0.160
135 (MAX)	3.70	0.380	0.160

- 2.7. SHOULD ANY OF THE SITE-SPECIFIC PARAMETERS BE HIGHER THAN WHAT IS NOTED ABOVE, THE EOR SHALL BE CONTACTED TO PROVIDE A REVISED DESIGN.
3. FOUNDATIONS ARE DESIGNED BY OTHERS, FLOCK SAFETY SHALL PROVIDE THE CONTRACTOR WITH INSTALLATION SPECIFICATIONS AND GUIDELINES. CONTRACTOR IS RESPONSIBLE FOR VERIFYING SOIL CONDITIONS PRIOR TO INSTALLATION.


GENERAL & CONSTRUCTION NOTES

- 1. CONTRACTOR SHALL CONTACT DESIGNATED AGENCY TO LOCATE ALL UNDERGROUND UTILITIES PRIOR TO CONSTRUCTION.
- 2. CONTRACTOR SHALL APPLY AND OBTAIN AN APPROVED TRAFFIC CONTROL PLAN IN ACCORDANCE WITH MUTCD AND LOCAL JURISDICTION STANDARDS.
- 3. CONTRACTOR SHALL RESTORE ALL DISTURBED AREAS TO ORIGINAL SITE CONDITION TO THE SATISFACTION OF STATE DEPARTMENT OF TRANSPORTATION AND LOCAL JURISDICTION.
- 4. ALL WORK SHALL CONFORM TO APPLICABLE ELECTRICAL CODES EXCEPT WHEN STATE DEPARTMENT OF TRANSPORTATION OR LOCAL JURISDICTION STANDARDS SUPERSEDE.
- 5. ALL CONSTRUCTION SHALL BE IN ACCORDANCE WITH SPECIFICATIONS DEFINED BY THE STATE DEPARTMENT OF TRANSPORTATION OR LOCAL JURISDICTION, UNLESS SPECIFICALLY STATED OR SHOWN OTHERWISE HEREIN.

ADA COMPLIANCE NOTES

- 1. ALL SIDEWALK CONSTRUCTION SHALL BE IN ACCORDANCE WITH ADA TITLE II, STATE DEPARTMENT OF TRANSPORTATION, AND LOCAL JURISDICTION STANDARDS,
- 2. STATE DEPARTMENT OF TRANSPORTATION CURRENT EDITION STANDARDS SHALL BE USED FOR PEDESTRIAN CONTROL PLANS WHEN CLOSURE OF SIDEWALK IS REQUIRED FOR CONSTRUCTION.
- 3. MINIMUM CLEAR PEDESTRIAN ACCESS ROUTE (PAR) SHALL BE 48" WIDE.
- 4. NO OBSTRUCTION IS PERMITTED ALONG THE WIDTH OF THE SIDEWALK. UP TO AN ELEVATION OD 7'-0" ABOVE GRADE.

ITEM NO.	PART NUMBER	DESCRIPTION	WEIGHT (LB)	QTY.
1	701-0059	FLOCK SAFETY CAMERA	3.6	1
2	201-00087	MOUNTING CLAMP	1.0	1
3	205-00010	60W SOLAR KIT	17.0	1
4	1020-01	STYLE 7 COUPLER ASSEMBLY	168.42	1

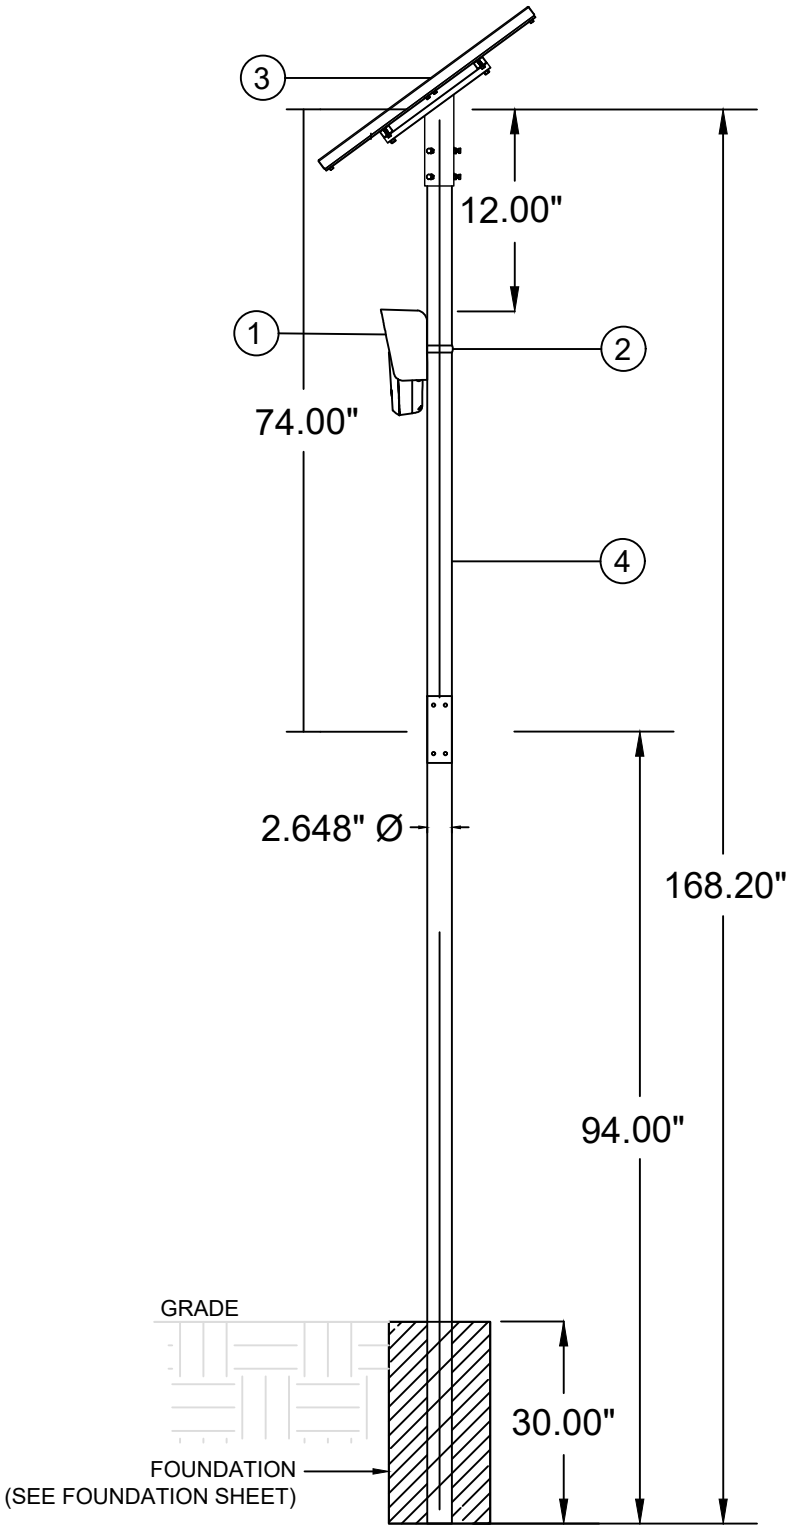

1 POLE ELEVATION DETAIL
SCALE: N/A

THIS DOCUMENT HAS BEEN DRAWN BASED OFF THE MOST RECENT AVAILABLE DATA & AERIAL IMAGERY. THIS INCLUDES RIGHT OF WAY, EXISTING UTILITIES, & PRIVATE PROPERTY LINES. IT REMAINS THE RESPONSIBILITY OF OTHERS TO VERIFY ALL DATA PRIOR AND EXISTING SURROUNDING FACILITIES TO VERIFY & CONFLICTS ABOVE & BELOW GRADE. ALL CONSTRUCTION TO FOLLOW XXXXXX GENERAL GUIDELINES. DO NOT SCALE DRAWINGS. CALL 811 PRIOR TO DIGGING.



REV	DESCRIPTION	DATE	BY


TITLE:	POLE DETAILS
SCOPE OF WORK:	COUNTY OF YUBA, CA ALPR CAMERA INSTALLATION

PLANS PREPARED BY:



PROJ#: 1441086

DRAWN BY:	JEEVESH OJHA
CHECKED BY:	GURKAMAL PREET SINGH
APPROVED BY:	CRYSTAL BRAUN
DATE: 12/24/2025	SHEET: 6 OF 8

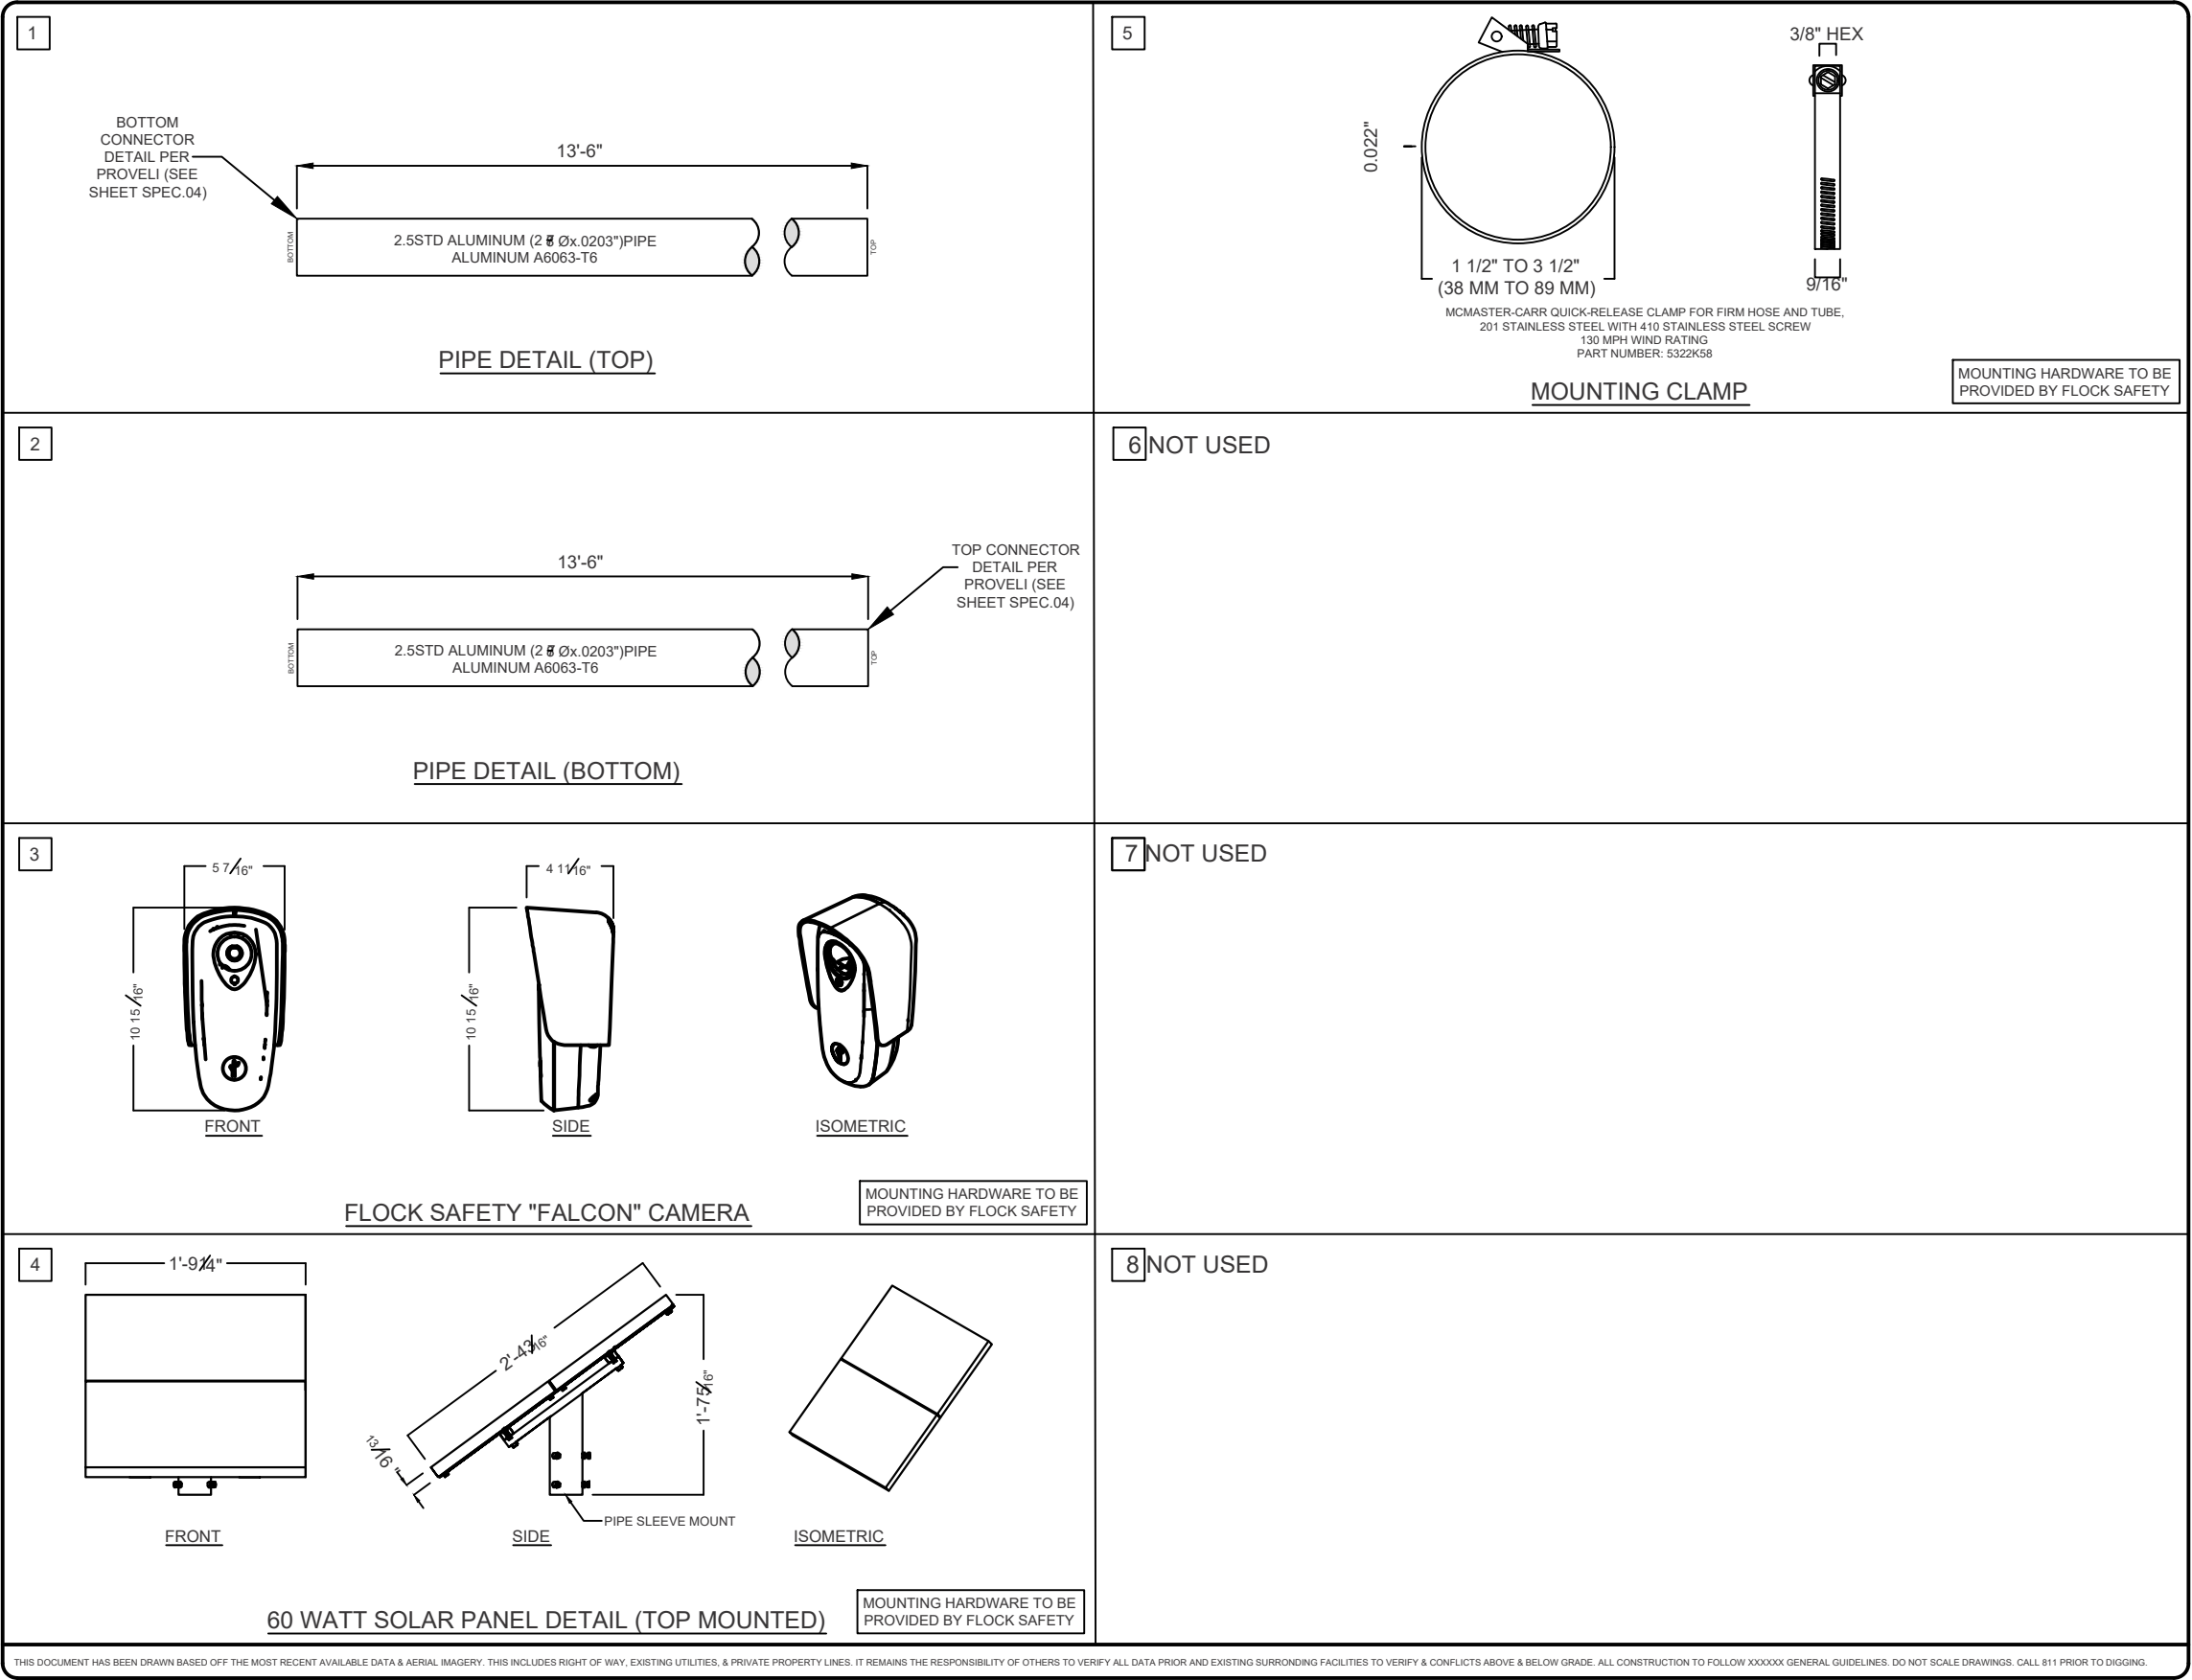

THIS DOCUMENT HAS BEEN DRAWN BASED OFF THE MOST RECENT AVAILABLE DATA & AERIAL IMAGERY. THIS INCLUDES RIGHT OF WAY, EXISTING UTILITIES, & PRIVATE PROPERTY LINES. IT REMAINS THE RESPONSIBILITY OF OTHERS TO VERIFY ALL DATA PRIOR AND EXISTING SURROUNDING FACILITIES TO VERIFY & CONFLICTS ABOVE & BELOW GRADE. ALL CONSTRUCTION TO FOLLOW XXXXXX GENERAL GUIDELINES. DO NOT SCALE DRAWINGS. CALL 811 PRIOR TO DIGGING.

REV	DESCRIPTION	DATE	BY

TITLE:	POLE DETAILS
SCOPE OF WORK:	COUNTY OF YUBA, CA ALPR CAMERA INSTALLATION

PLANS PREPARED BY:	
 A CONGRUEX COMPANY	
PO Box 59028 Norwalk, CA 90652 (949) 250-0004	

PROJ#:	1441086
DRAWN BY:	JEEVESH OJHA
CHECKED BY:	GURKAMAL PREET SINGH
APPROVED BY:	CRYSTAL BRAUN
DATE:	12/24/2025
SHEET:	7 OF 8

ITEM NO.	DESCRIPTION	QTY.
1	2.5" SCH 40 2.875OD 74.000L	1
2	2.5 SCH 40 2.875OD 94.000L	1
3	BUT TORX 0.250-20 TAMPER-RESISTANT	6
4	INSERT SLEEVE STYLE 7 TAPPED	1
5	ORING	1
6	WASHER	6
7	CONCRETE FOOTING	1
8	HBOLT 0.2500-20	1

PROVELI STYLE 7 COUPLER ASSEMBLY







PART #: 1020-01

MATERIAL: VARIES

WEIGHT: 168.42 LBS

DATE: 09/27/2023

DO NOT SCALE DRAWINGS (NTS)

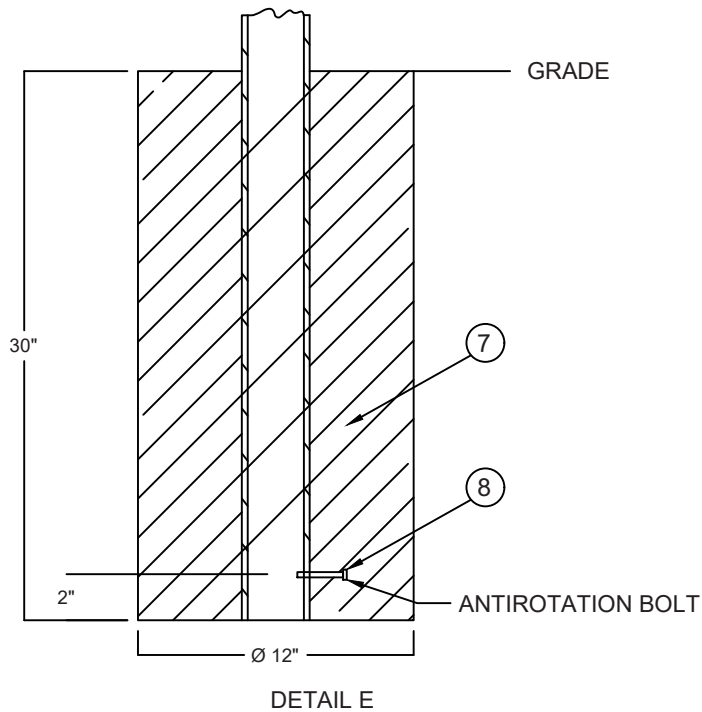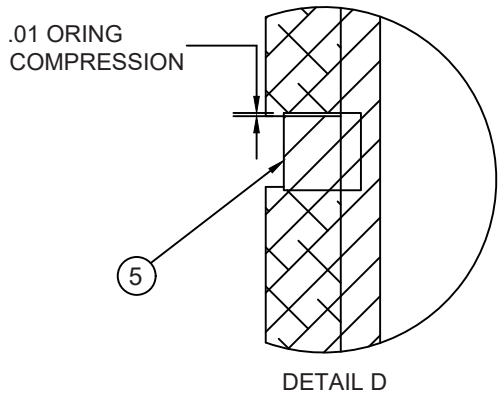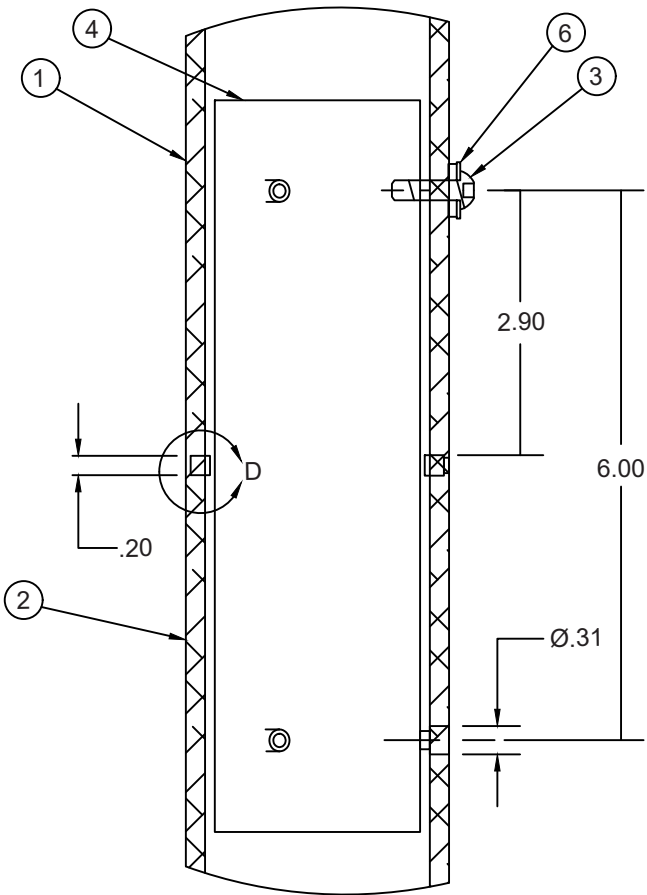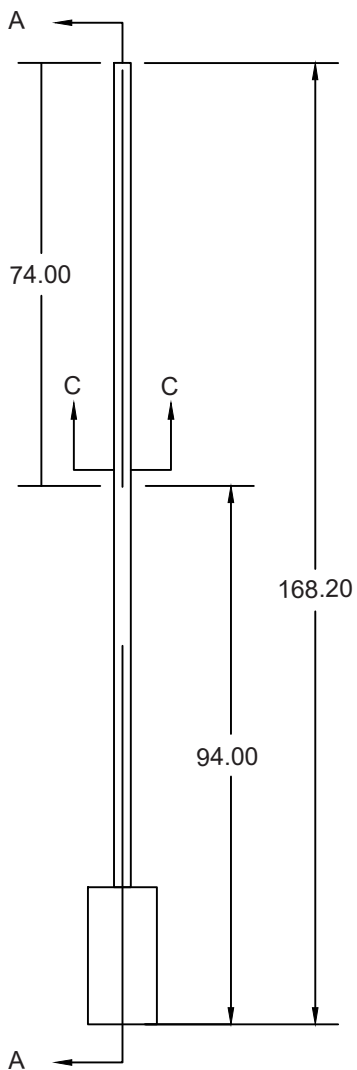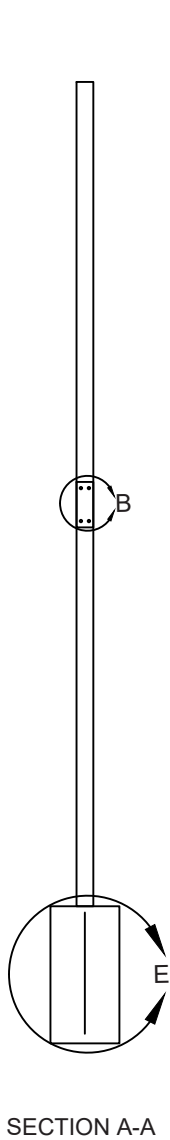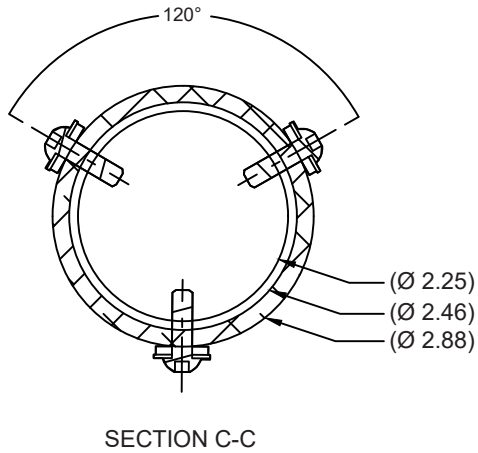

THIS DOCUMENT HAS BEEN DRAWN BASED OFF THE MOST RECENT AVAILABLE DATA & AERIAL IMAGERY. THIS INCLUDES RIGHT OF WAY, EXISTING UTILITIES, & PRIVATE PROPERTY LINES. IT REMAINS THE RESPONSIBILITY OF OTHERS TO VERIFY ALL DATA PRIOR AND EXISTING SURROUNDING FACILITIES TO VERIFY & CONFLICTS ABOVE & BELOW GRADE. ALL CONSTRUCTION TO FOLLOW XXXXXX GENERAL GUIDELINES. DO NOT SCALE DRAWINGS. CALL 811 PRIOR TO DIGGING.

REV	DESCRIPTION	DATE	BY

TITLE:	POLE DETAILS
SCOPE OF WORK:	COUNTY OF YUBA, CA ALPR CAMERA INSTALLATION

PLANS PREPARED BY:

CHC
A CONGRUEX* COMPANY
PO Box 59028
Norwalk, CA 90652
(949) 250-0004

PROJ#: 1441086

DRAWN BY: JEEVESH OJHA
CHECKED BY: GURKAMAL PREET SINGH
APPROVED BY: CRYSTAL BRAUN
DATE: 12/24/2025 SHEET: 8 OF 8